


4 3 2 1

NOTICE
THIS DRAWING CONTAINS A PROPRIETARY DESIGN ASSIGNED TO SPIRA INTERNATIONAL, INC. ALL RIGHTS TO DUPLICATE, TRANSFER OR USE ARE EXPRESSLY RESERVED BY SPIRA INTERNATIONAL. THE BUYER IS LICENSED TO BUILD ONE ASSEMBLY FROM THESE PLANS.

REVISIONS				
ZONE	LTR	DESCRIPTION	DATE	APPROVED
	B	ADDED SPECIFICATIONS TABLE	02/09/14	JJS

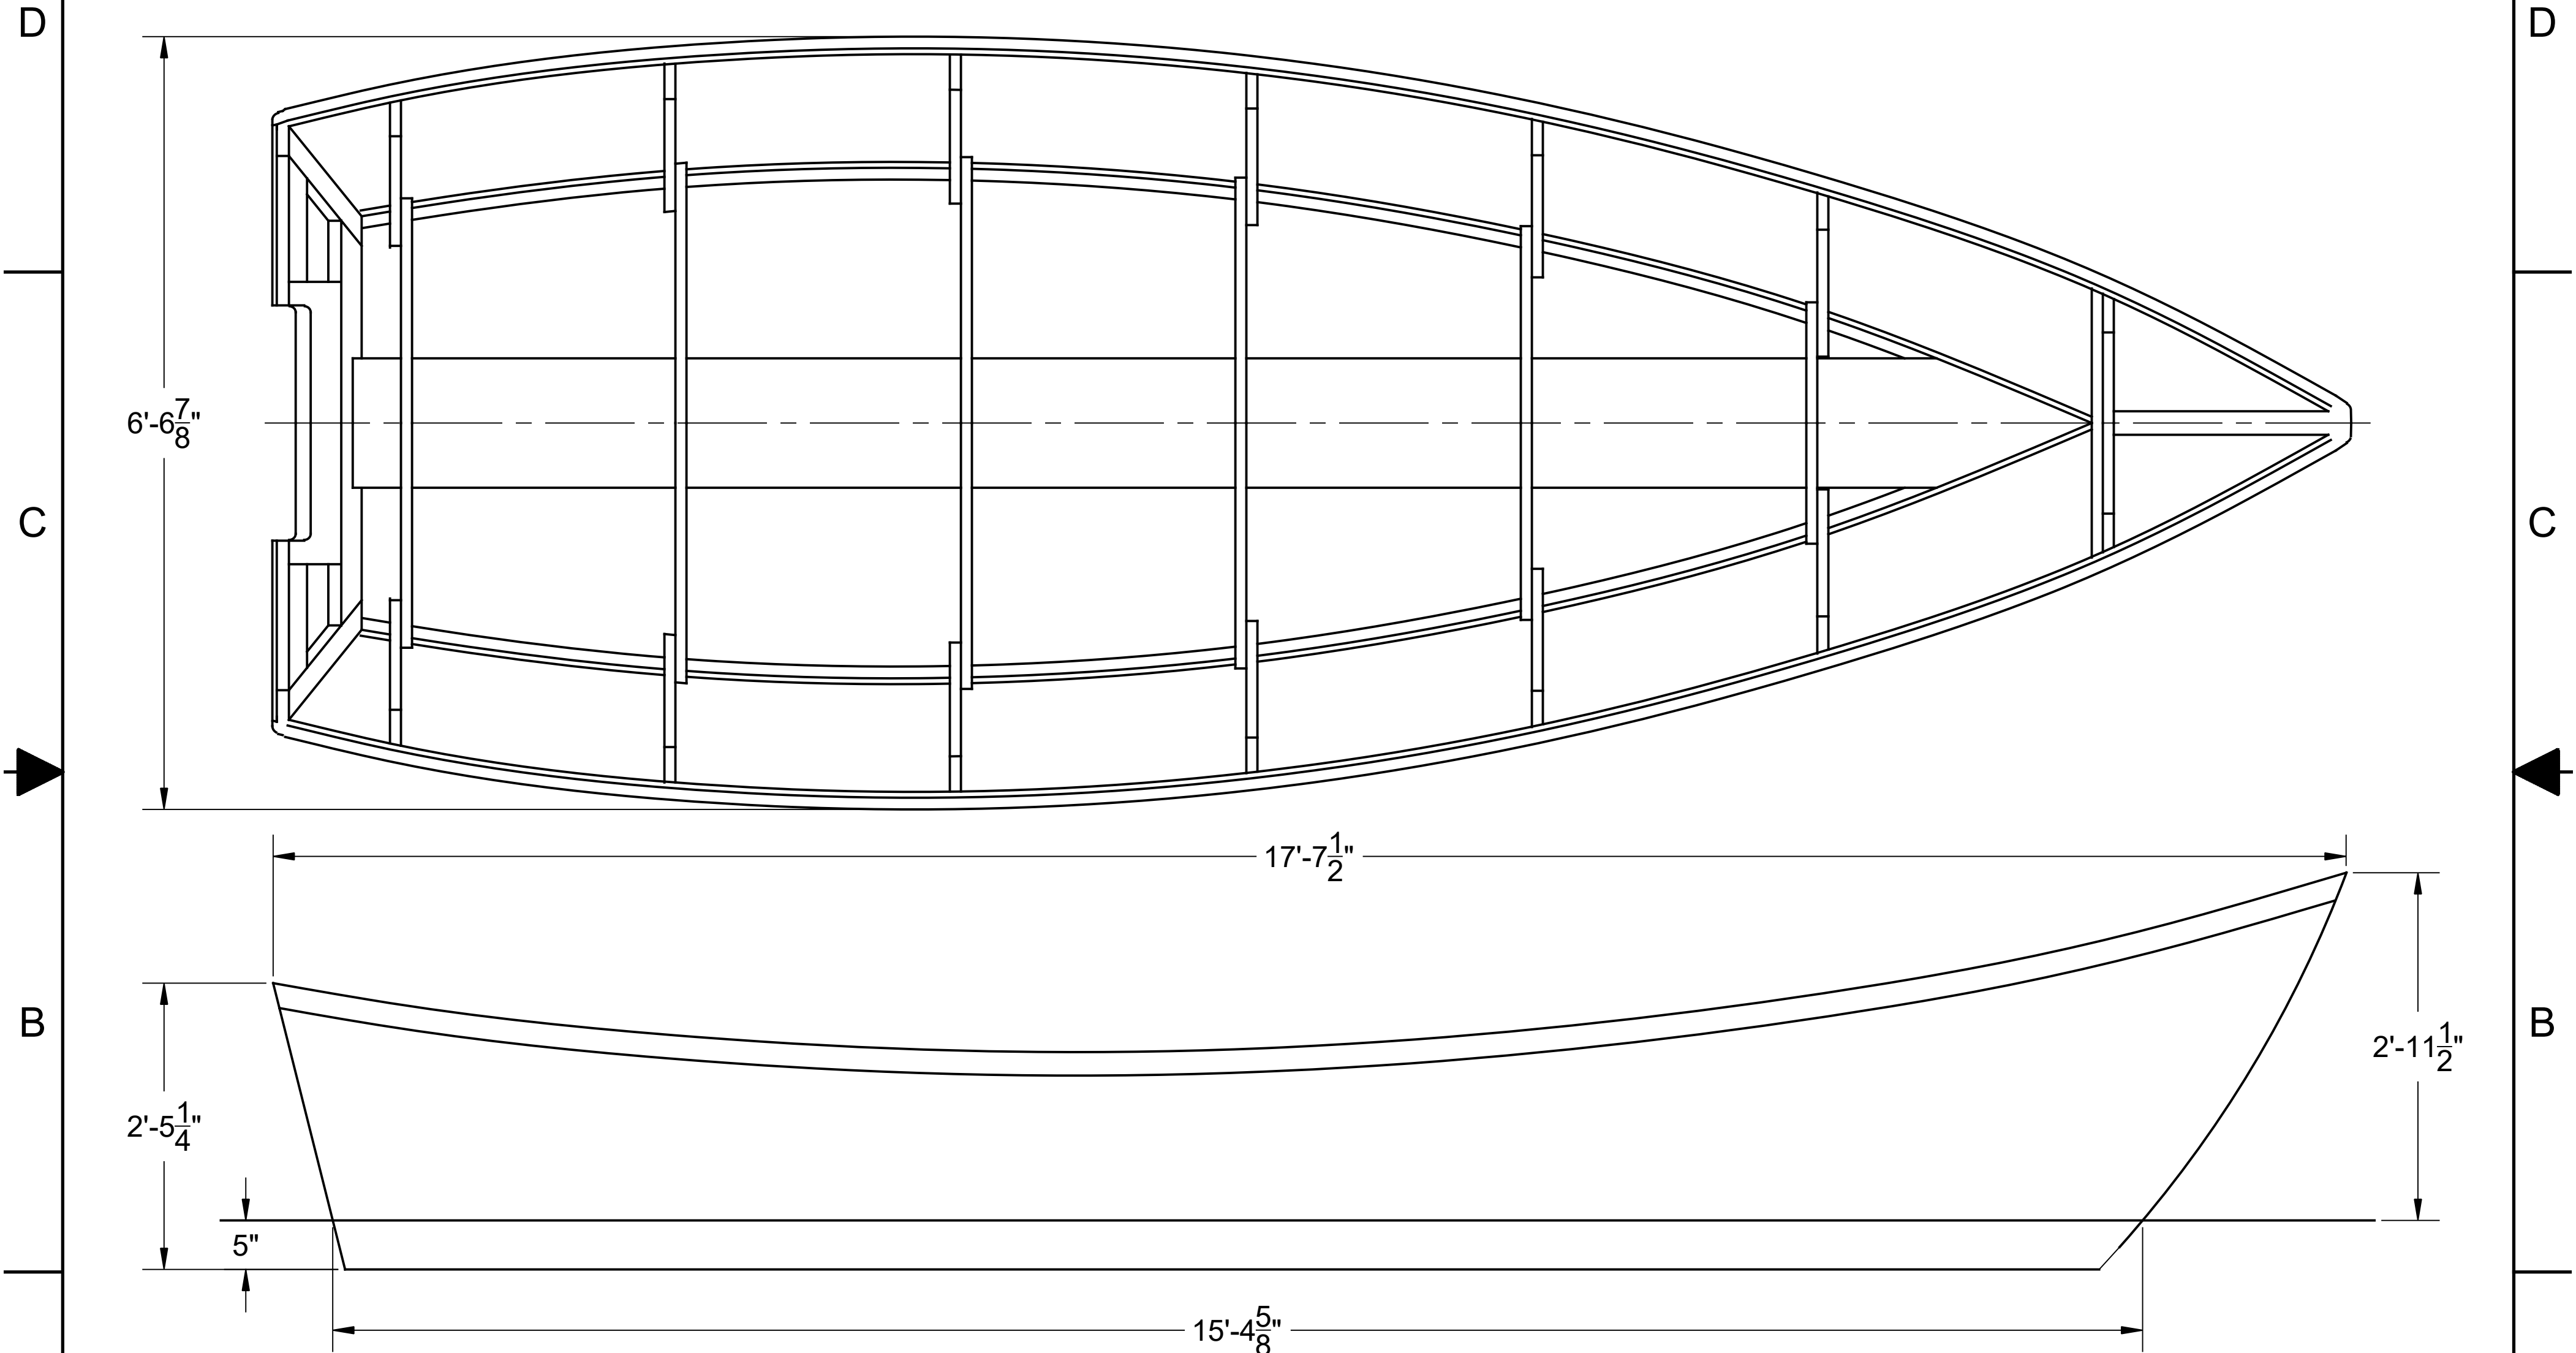

SPECIFICATIONS	
MAX. DISPLACEMENT	2550 LBS
HULL WEIGHT	650 LBS
MAX. HP - 20" REMOTE	75 HP
MAX HP - 15" TILLER	30 HP

 Spira International, Inc. Huntington Beach, California	
CAROLINIAN 18' CAROLINA DORY	
DRAWN BY: J. SPIRA	DATE: 07/05/00
DRAWING NO. CARO01	
SCALE 1" = 1'	SHEET OF

4

3

2

1

NOTICE

THIS DRAWING CONTAINS A PROPRIETARY DESIGN ASSIGNED TO SPIRA INTERNATIONAL, INC. ALL RIGHTS TO DUPLICATE, TRANSFER OR USE ARE EXPRESSLY RESERVED BY SPIRA INTERNATIONAL. THE BUYER IS LICENSED TO BUILD ONE ASSEMBLY FROM THESE PLANS.

REVISIONS				
ZONE	LTR	DESCRIPTION	DATE	APPROVED
	C	ADDED FASTENING SCHEDULE	02/09/14	JJS

BILL OF MATERIALS

6 SHEETS 1/2" PLY
80' 2X4 LUMBER FOR FRAMES (1X4 OPTIONAL)
130' 1X2 CLEAR LUMBER FOR SHEER CLAMP, CHINE LOG AND RUB RAILS
17' 2X6 LUMBER FOR KEELSON
9' 2X8 LUMBER FOR TRANSOM AND STEM
60 #10 X 2 1/2 SS DECK SCREWS
120 #8 X 2 SS DECK SCREWS
600 #8 X 1-1/2 SS DECK SCREWS
1-1/2 GAL EPOXY RESIN
17 YDS 6 OZ FIBERGLASS CLOTH

FASTENING SCHEDULE

FRAME TO FRAME: #10 X 2 -1/2 DECK SCREWS
PLANKING TO FRAME: #8 X 1-1/2 DECK SCREWS
LONGITUDINAL TO FRAME: #8 X 2 DECK SCREWS

NOTES:

1. YOU MAY SCARF TOGETHER SHORTER PIECES TO CREATE THE LONGITUDINAL ELEMENTS.
2. NOMINAL LUMBER SIZED CALLED OUT, E.G. A 2 X 4 LUMBER IS ACTUAL SIZE 1-1/2" X 3-1/2"



Spira International, Inc.
Huntington Beach, California

CAROLINIAN
18' CAROLINA DORY

DRAWN BY:
J. SPIRA



DATE:
07/06/00

DRAWING NO.

CARO02

SCALE 1/5 & NOTED

SHEET OF

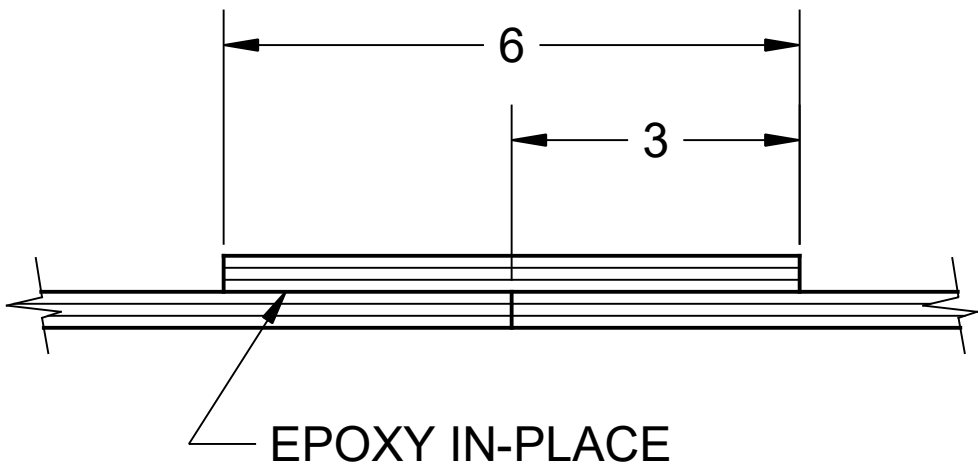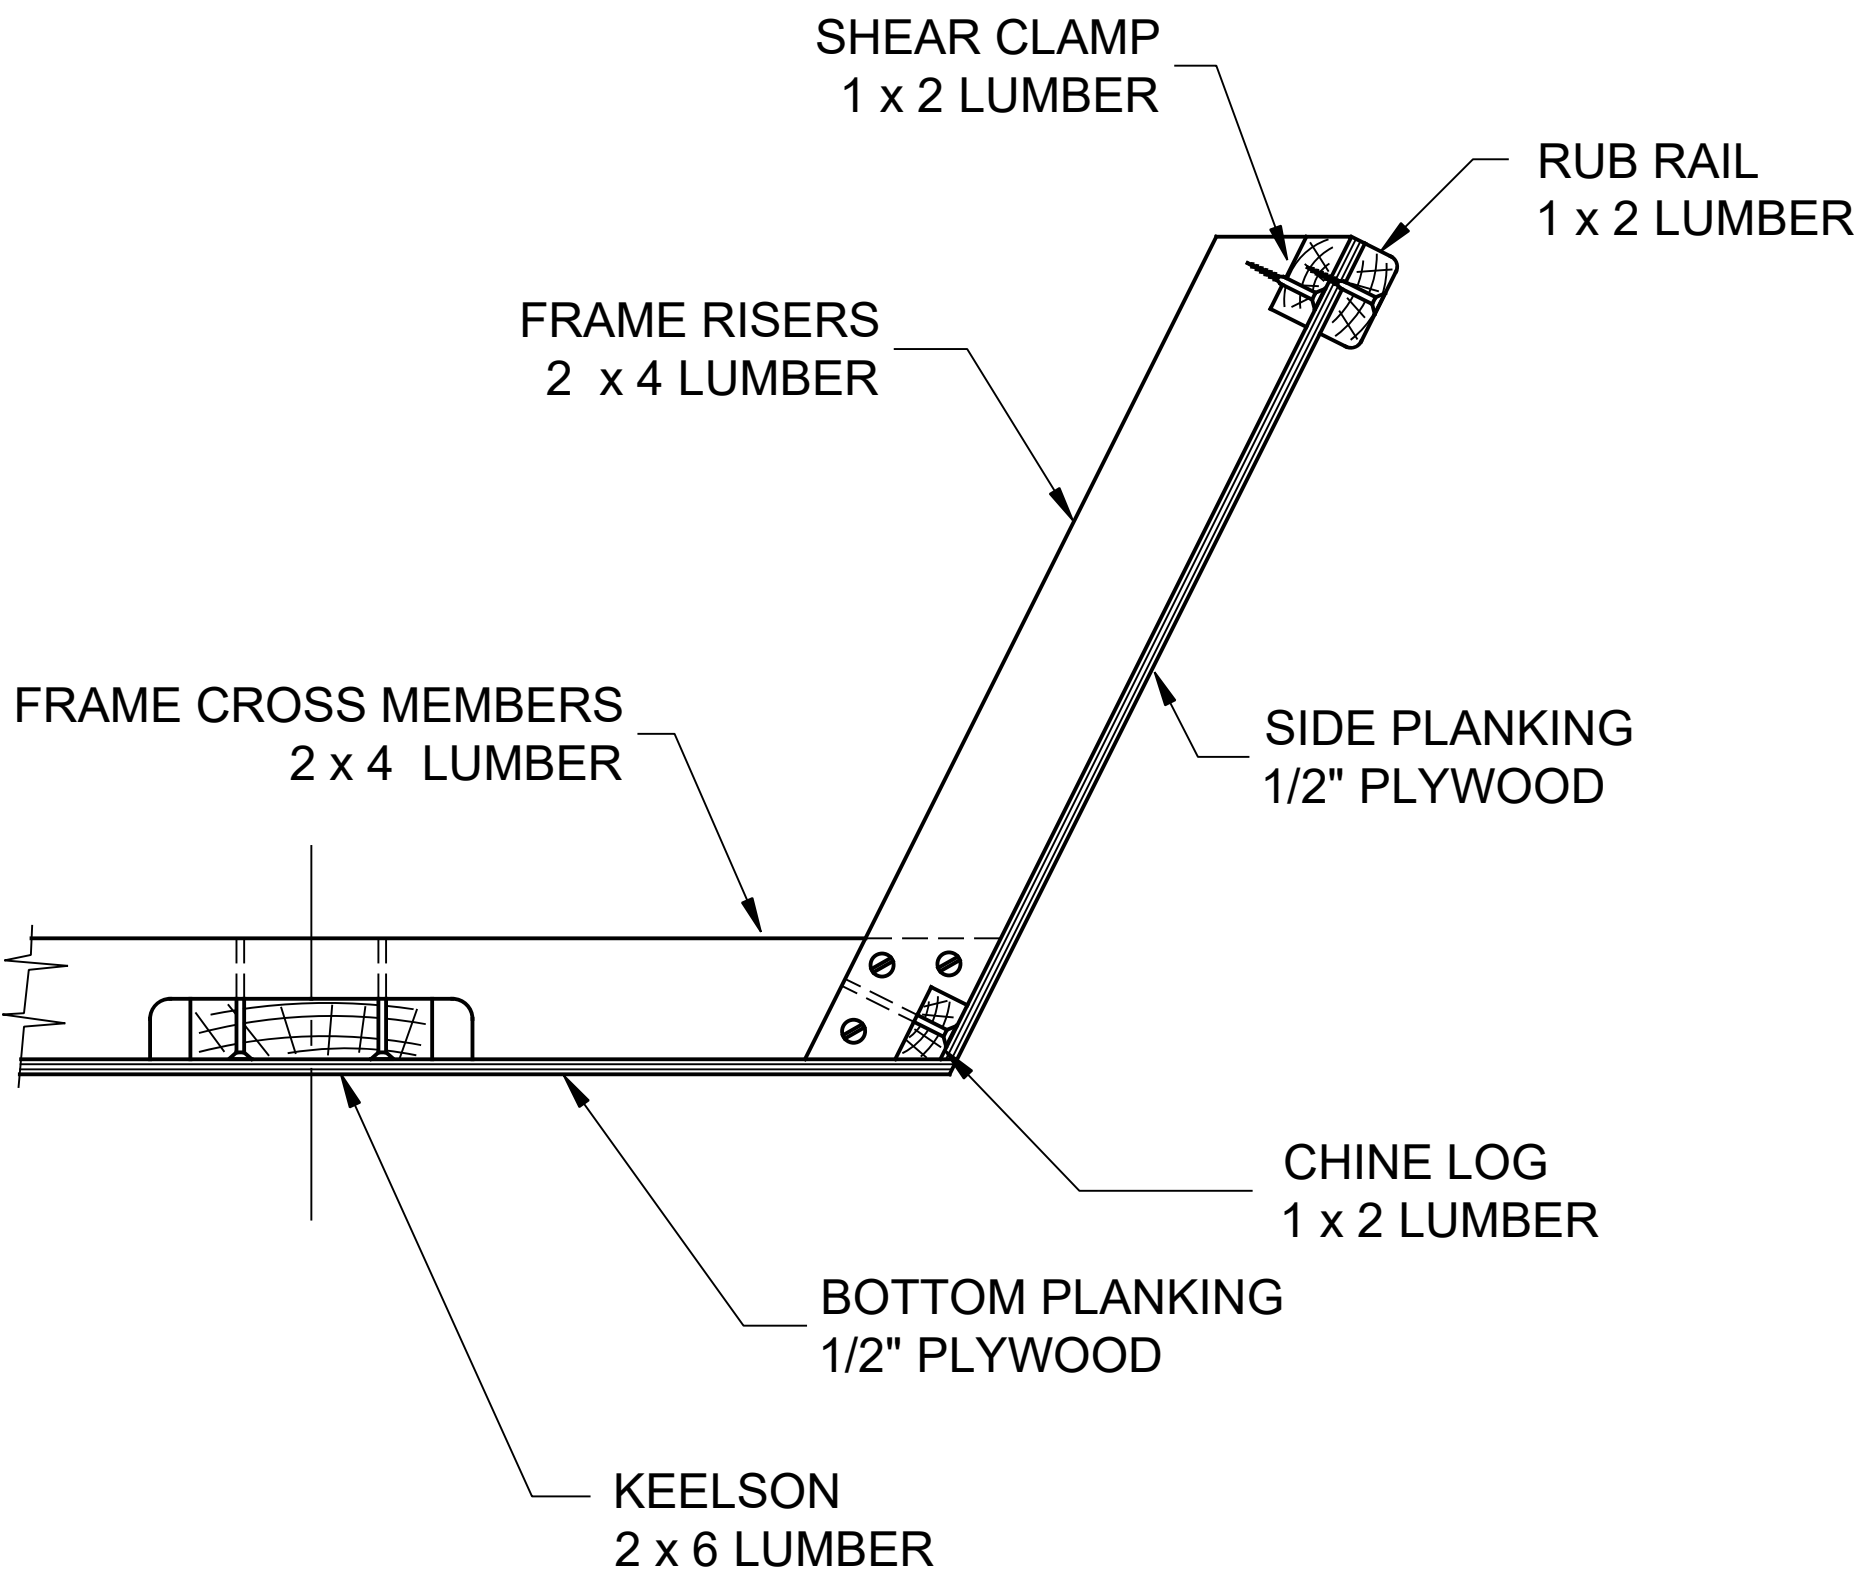

BUTT BLOCKS REQUIRED
AT ALL PLYWOOD SEAMS
(BLOCK ON INSIDE OF HULL)