

4

3


2

1

NOTICE

THIS DRAWING CONTAINS A PROPRIETARY DESIGN ASSIGNED TO SPIRA INTERNATIONAL, INC. ALL RIGHTS TO DUPLICATE, TRANSFER OR USE ARE EXPRESSLY RESERVED BY SPIRA INTERNATIONAL. THE BUYER IS LICENSED TO BUILD ONE ASSEMBLY FROM THESE PLANS.

REVISIONS				
ZONE	LTR	DESCRIPTION	DATE	APPROVED
	D	ADDED DRAFT	01/31/15	JJS

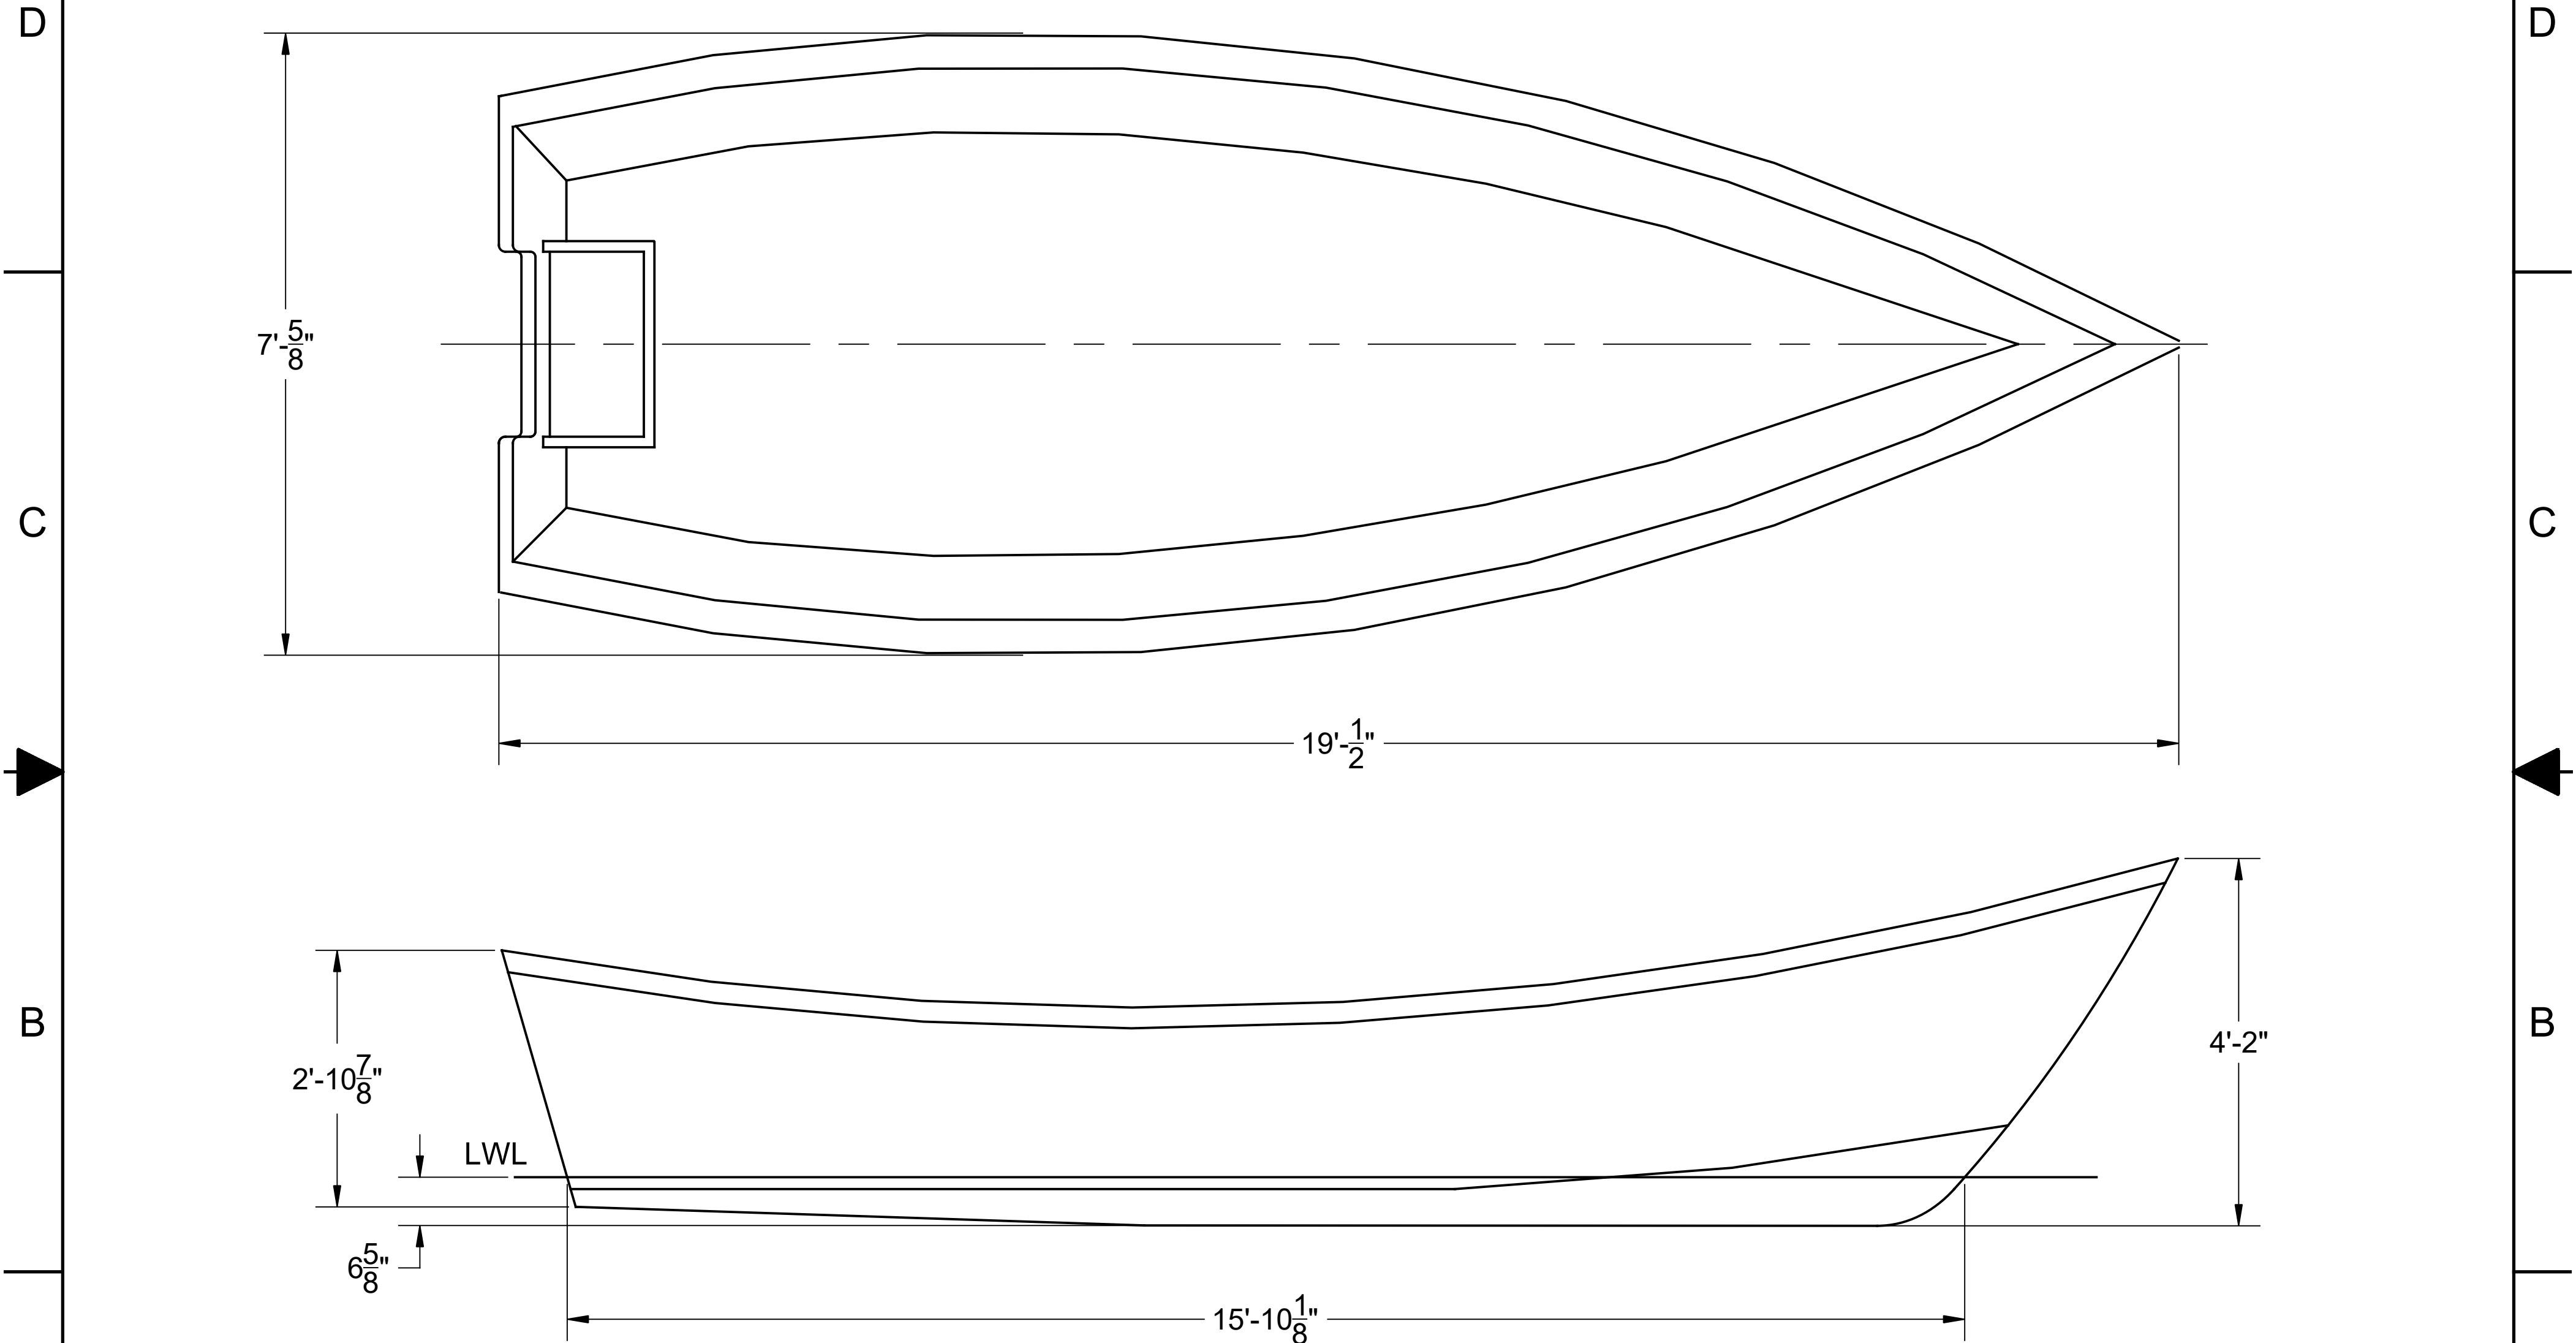

SPECIFICATIONS	
MAX. DISPLACEMENT	4000 LBS
HULL WEIGHT	1200 LBS
CALC. MAX. HORSEPOWER	125 HP
RECOMMENDED HP	75 HP



Spira International, Inc.
Huntington Beach, California

HATTERAS
19' V-BOTTOM CAROLINA DORY

DRAWN BY:
J. SPIRA

DATE:
02/16/04

DRAWING NO.
HATT01

SCALE 3/4" = 1'

SHEET OF

4

3


2

1

NOTICE

THIS DRAWING CONTAINS A PROPRIETARY DESIGN ASSIGNED TO SPIRA INTERNATIONAL, INC. ALL RIGHTS TO DUPLICATE, TRANSFER OR USE ARE EXPRESSLY RESERVED BY SPIRA INTERNATIONAL. THE BUYER IS LICENSED TO BUILD ONE ASSEMBLY FROM THESE PLANS.

REVISIONS				
ZONE	LTR	DESCRIPTION	DATE	APPROVED
	C	REVISED AND UPDATED	2/16/14	JJS

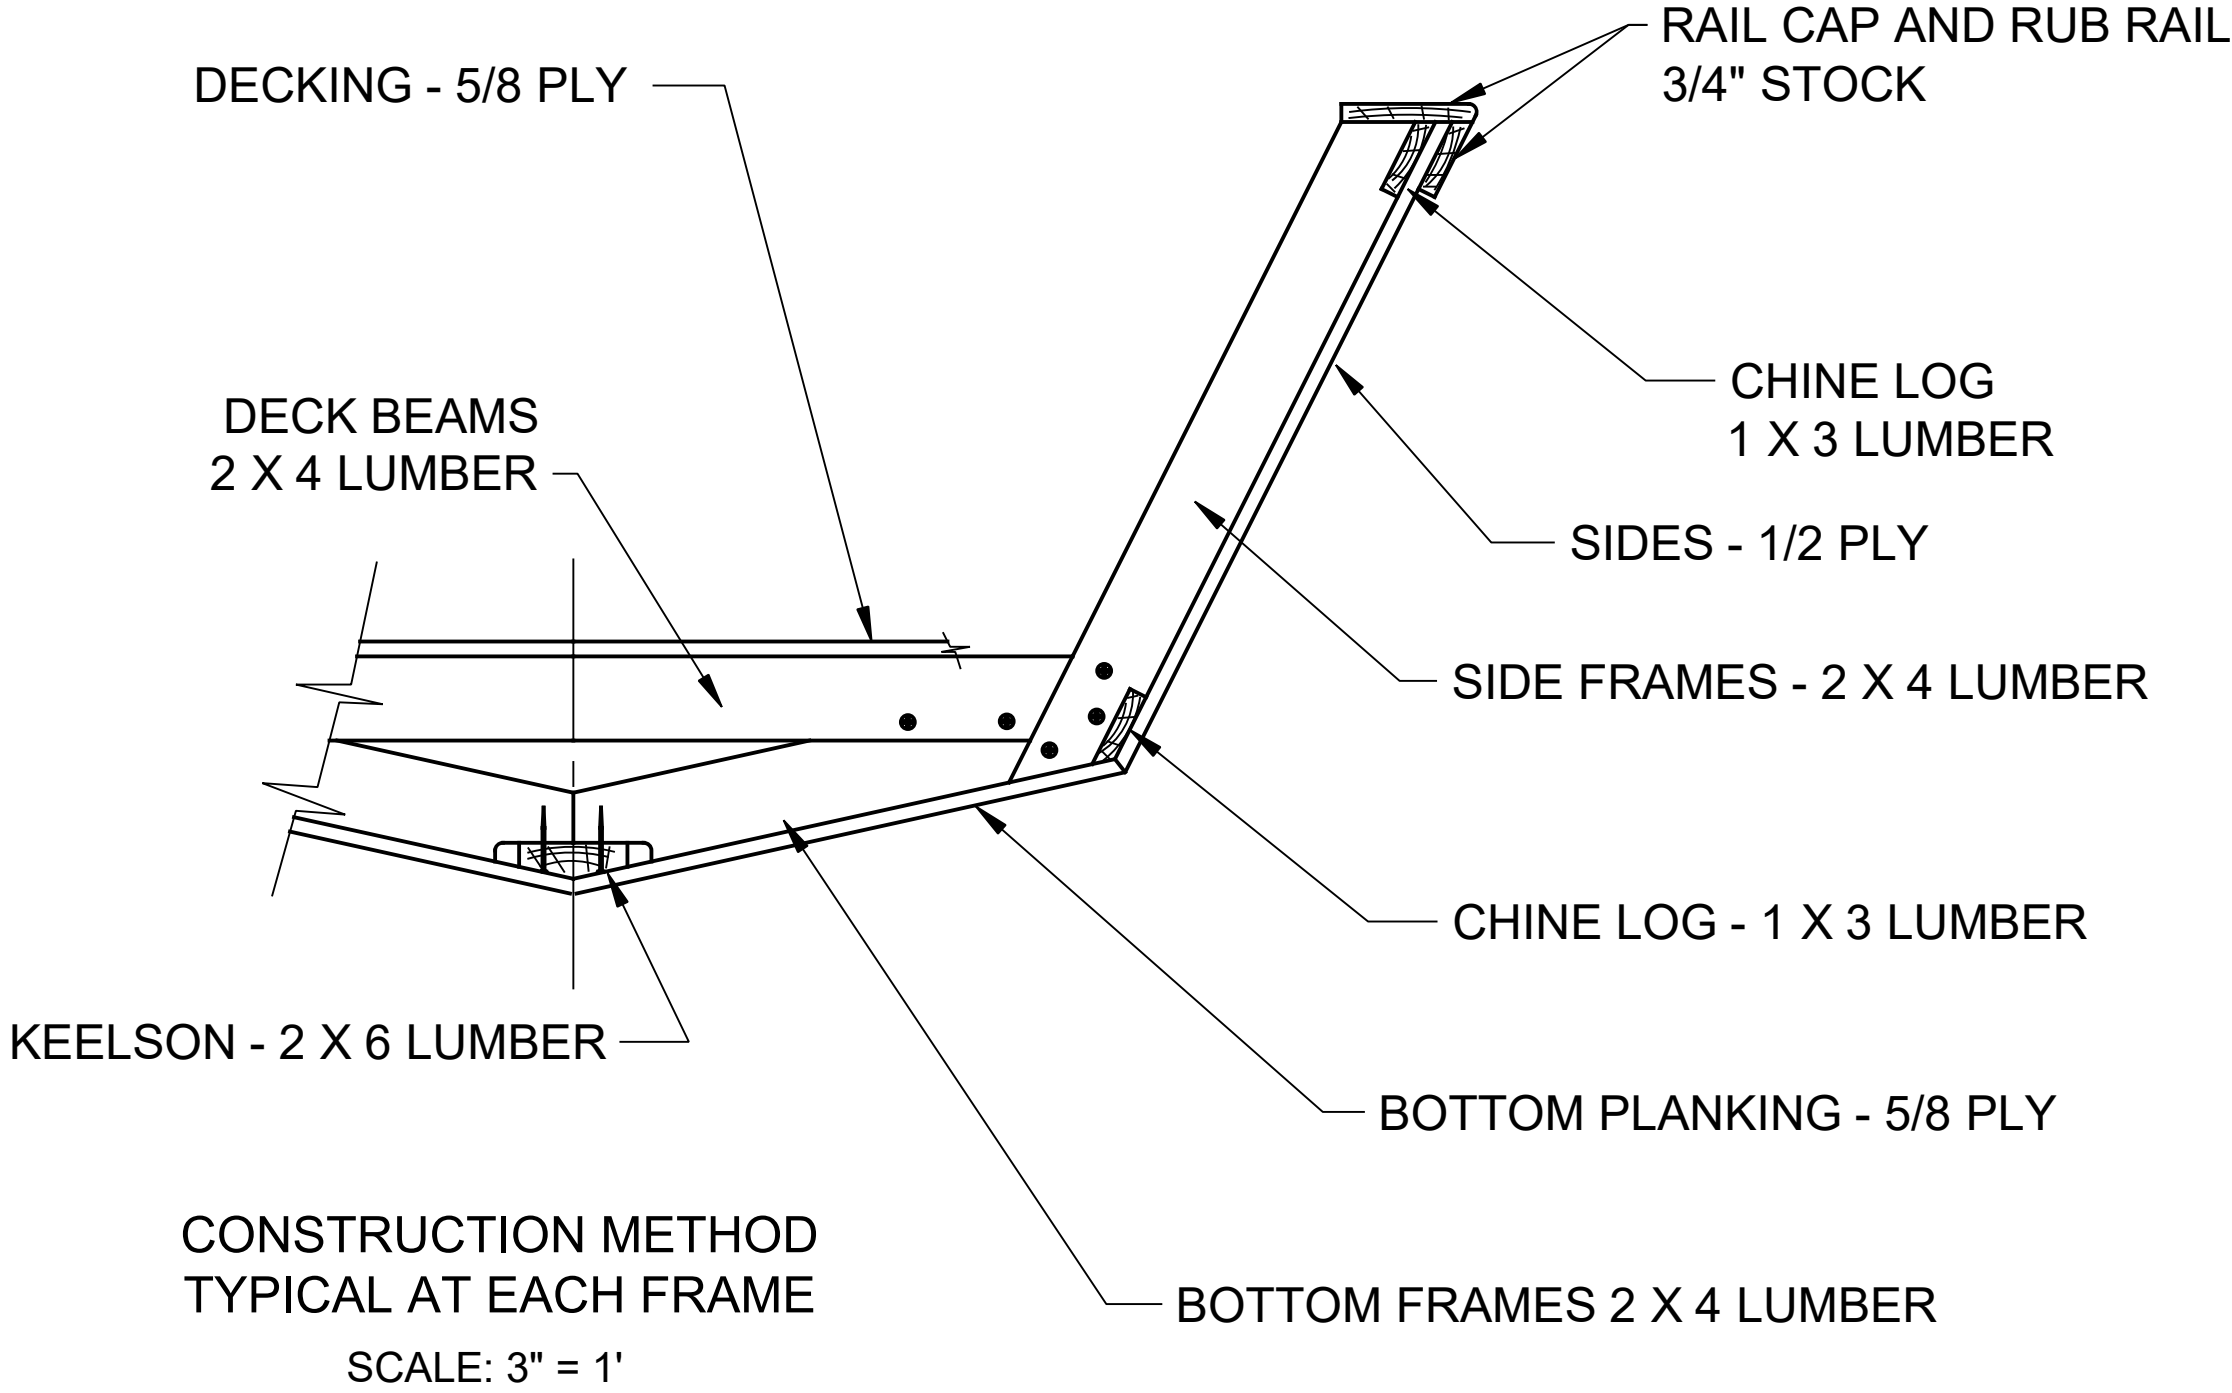

BILL OF MATERIALS (HULL ONLY)

8 SHEETS 5/8" PLY
6 SHEETS 1/2" PLY
140' 2X4 LUMBER FOR FRAMES
120' 1X3 CLEAR LUMBER FOR SHEER
CLAMP, CHINE LOG AND RUB RAILS
24' 2X6 LUMBER FOR KEELSON AND STEM
8' 2X8 LUMBER FOR TRANSOM & STEM KNEE
200 #10 X 2-1/2 SS DECK SCREWS
200 #8 X 2 SS DECK SCREWS
1000 #8 X 1-1/2 SS DECK SCREWS
3 GAL EPOXY RESIN
30 YDS - 6 OZ FIBERGLASS CLOTH (50" WIDE)

FASTENING SCHEDULE


2x FRAME TO 2x FRAME: #10 X 2 -1/2 DECK SCREWS
LONGITUDINAL TO FRAME: #8 X 2 DECK SCREWS
PLANKING TO FRAME: #8 X 1-1/2 DECK SCREWS

NOTES:


1. YOU MAY SCARF TOGETHER SHORTER PIECES TO CREATE THE LONGITUDINAL ELEMENTS.
2. NOMINAL LUMBER SIZED CALLED OUT, E.G. A 2 X 4 LUMBER IS ACTUAL SIZE 1-1/2" X 3-1/2"

SEQUENCE FOR MAKING FRAMES


NO SCALE

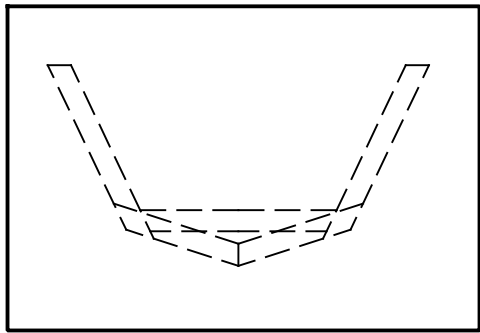


DRAW FRAME ON
SCRAP PLYWOOD

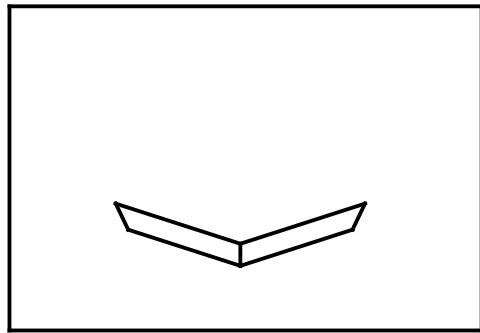


CUT OUT LOWER FRAME
ELEMENTS AND LOCATE
IN POSITION - EPOXY
CENTER JOINT

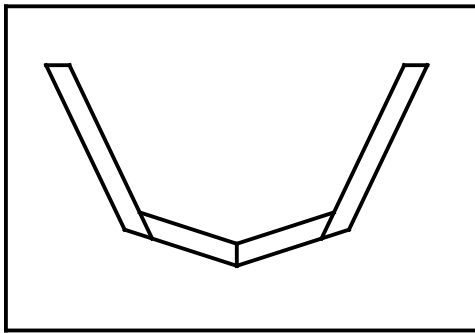

REPEAT FOR SIDE
FRAMES - EPOXY &
SCREW IN POSITION
ATOP BOTTOM FRAMES

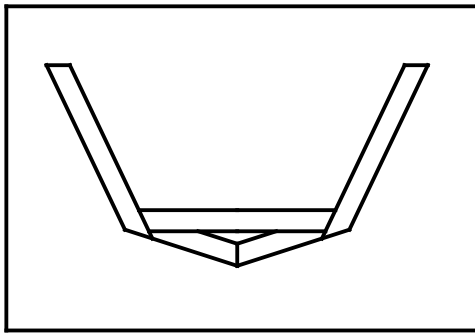

CUT OUT DECK
BEAM, LOCATE IN
POSITION, EPOXY &
SCREW IN PLACE

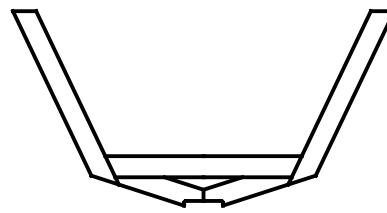

CUT OUT KEELSON
NOTCH AFTER EPOXY
HAS SET FULLY



Spira International, Inc.
Huntington Beach, California

HATTERAS
19' V-BOTTOM CAROLINA DORY

DRAWN BY:
J. SPIRA

DATE:
02/16/04

DRAWING NO.
HATT02

SCALE 3" = 1' & NOTED

SHEET OF